

The background of the entire image is a photograph of a large tree's trunk and branches against a clear blue sky. The trunk is thick and light-colored, leaning slightly to the right. The branches are bare, with small, round, brownish fruits or seed pods hanging from them.

{Between the boundaries}
PORTFOLIO
Architectural projects

by Yuanyuan LI

Birth: May 8, 1993

Qingdao Agricultural University, B.Engineering

apply for March I, UCLA

Contents



Endowing the olds with news.....	003
Between the books and the trees.....	11
Architecture park in the city.....	17
Urban design--rebuild of fishing port.....	21
Other work.....	25



[Endowing the old with the News]

The renewal of history district---a design of community center



Individual work

Location:Qingdao,China

People living in the history area have many problems for living. Their basic need can't be satisfied by the old facilities. The deficiency of green land, square and the public space have made negative effects on people's life.

As I start this design, I tried a lot of ways to solve these problems. In my point of view, the most important part of people's life is spending time in public space. Because in modern society, people feel more loneliness than in the past, especially the elder ones. In old city area, elders often live alone or with their partners, they have to stay at home because no proper place for them to have fun.

Visters' trace in the old city Local people's trace in the street

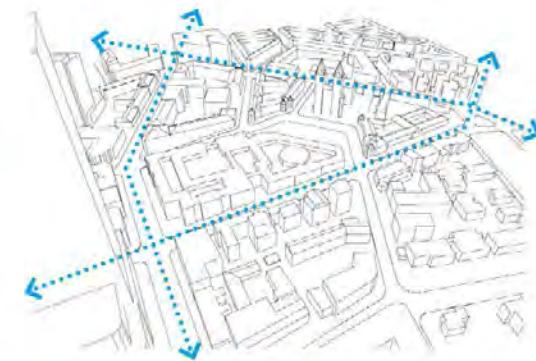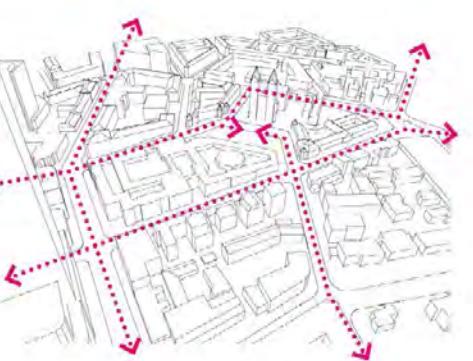

East facade



North facade




South facade




West facade

The Plaza with a church in this district, beautiful but can't satisfy the need of modern people

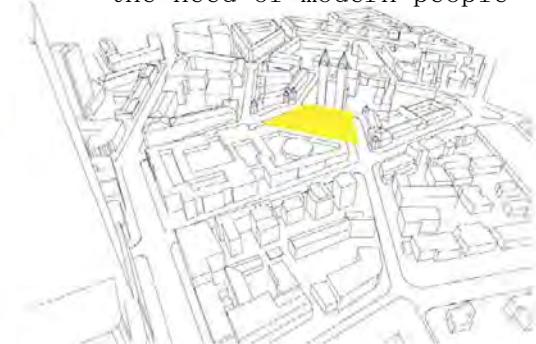





A-A section

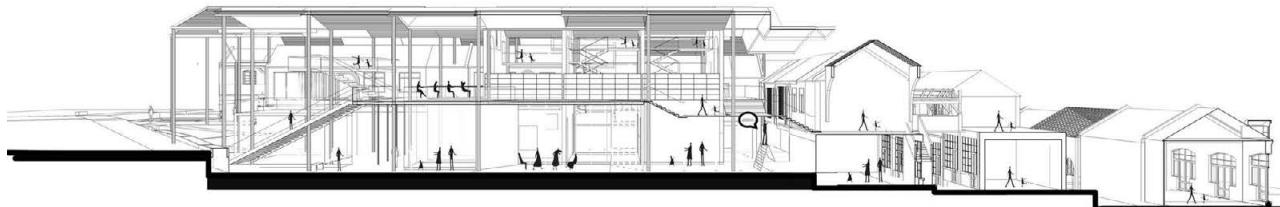

1-1 Section

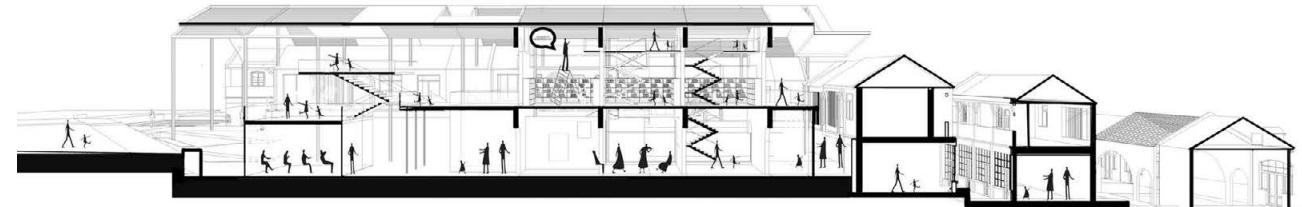

2-2 Section

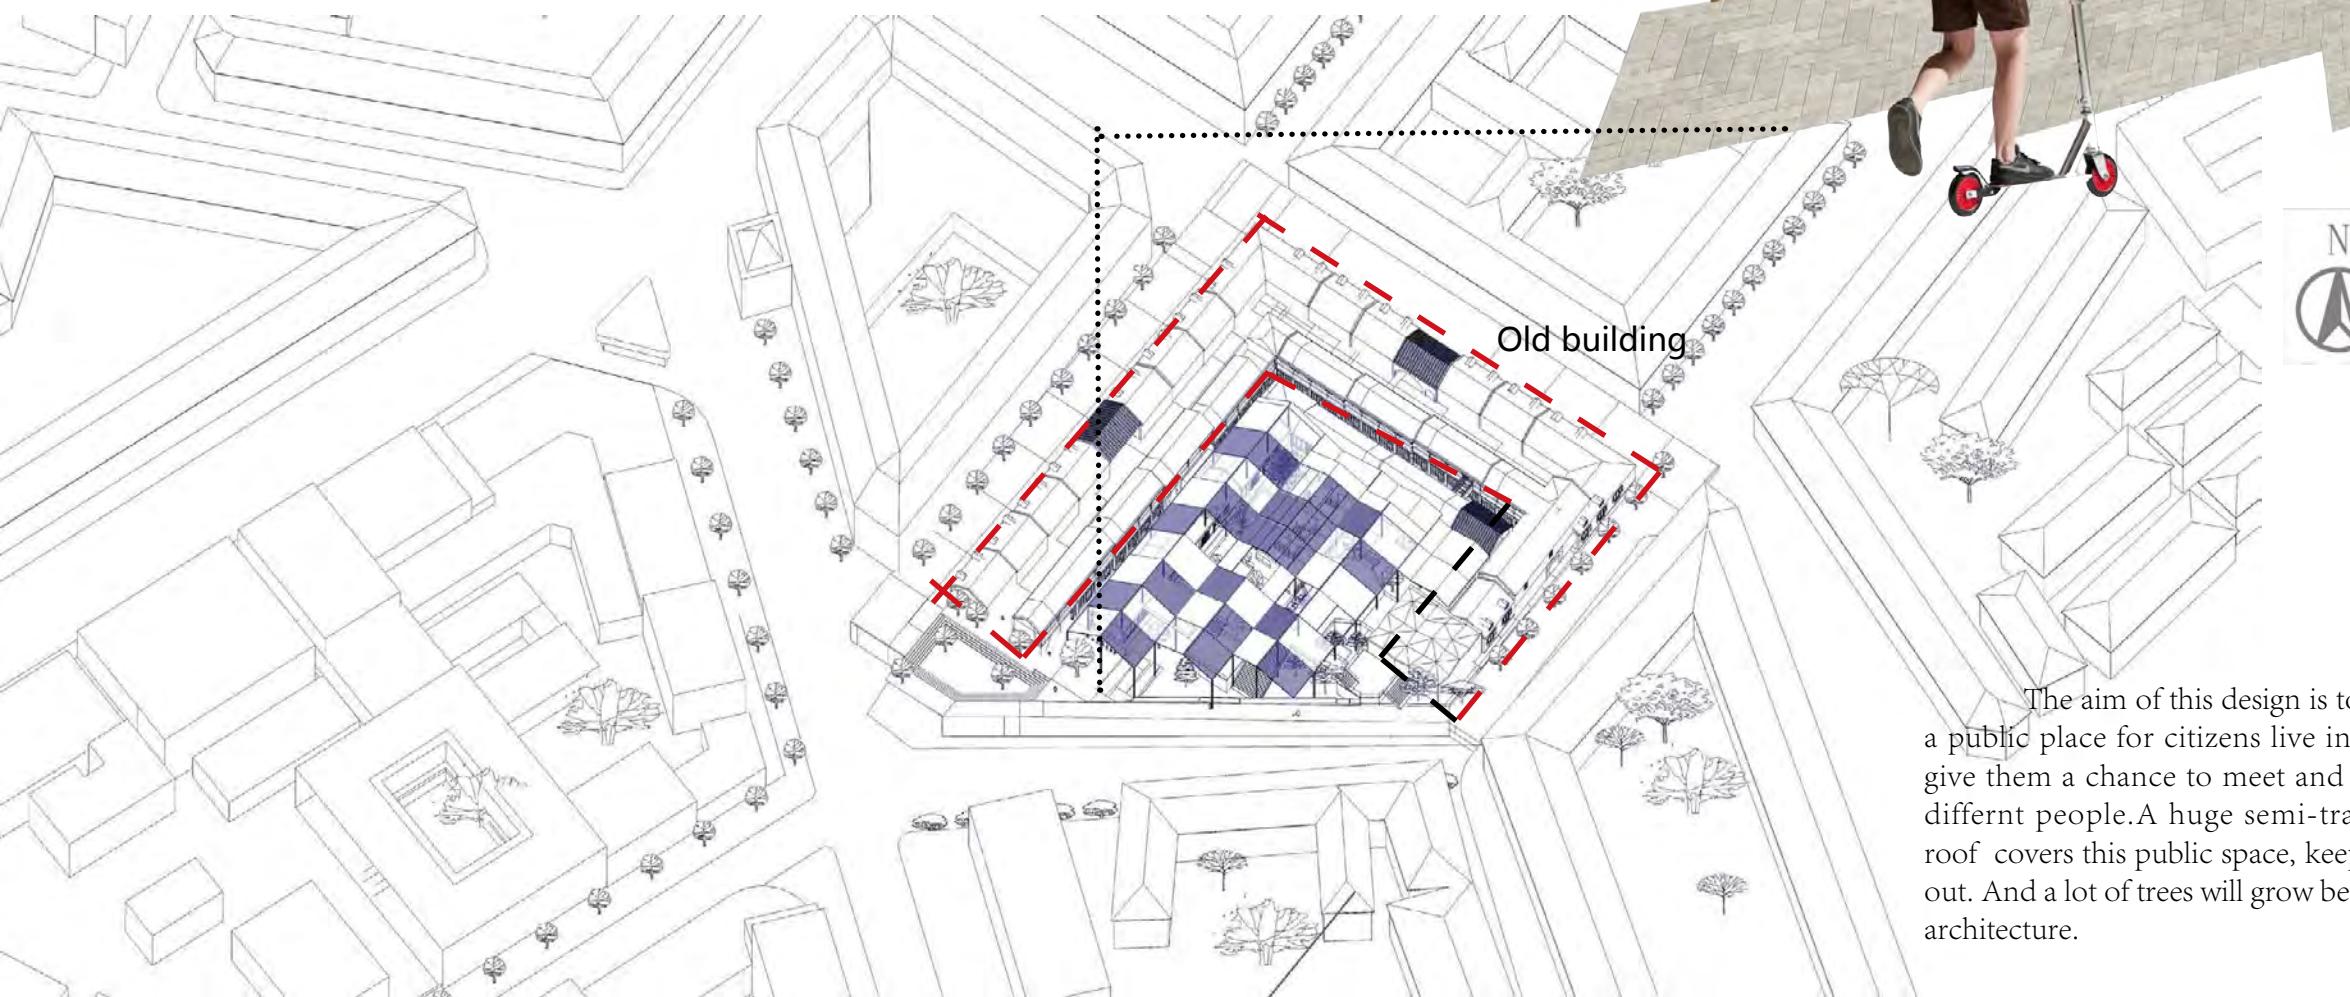

Old building



Old building

Old building


Old building

Old building

Old building

Old building


The aim of this design is to build a public place for citizens live in old city, give them a chance to meet and talked to different people. A huge semi-translucent roof covers this public space, keep the rain out. And a lot of trees will grow between the architecture.

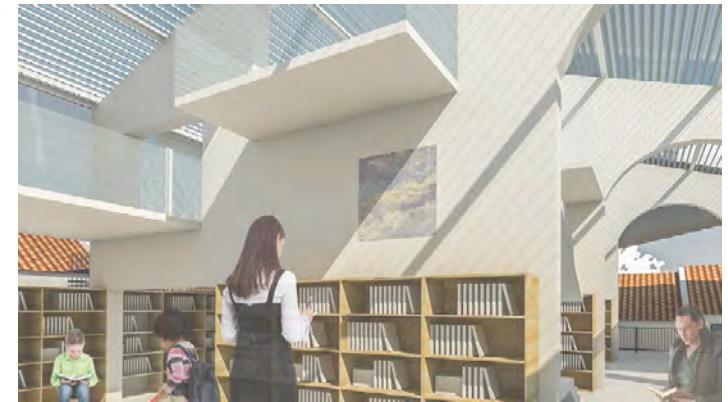




The old building used to be local people's home, but they are out dated as living house. So these space are designed to restaurant, store and hotel for tourists.

The new architecture is close to the old, people can see both of them in some perspective.

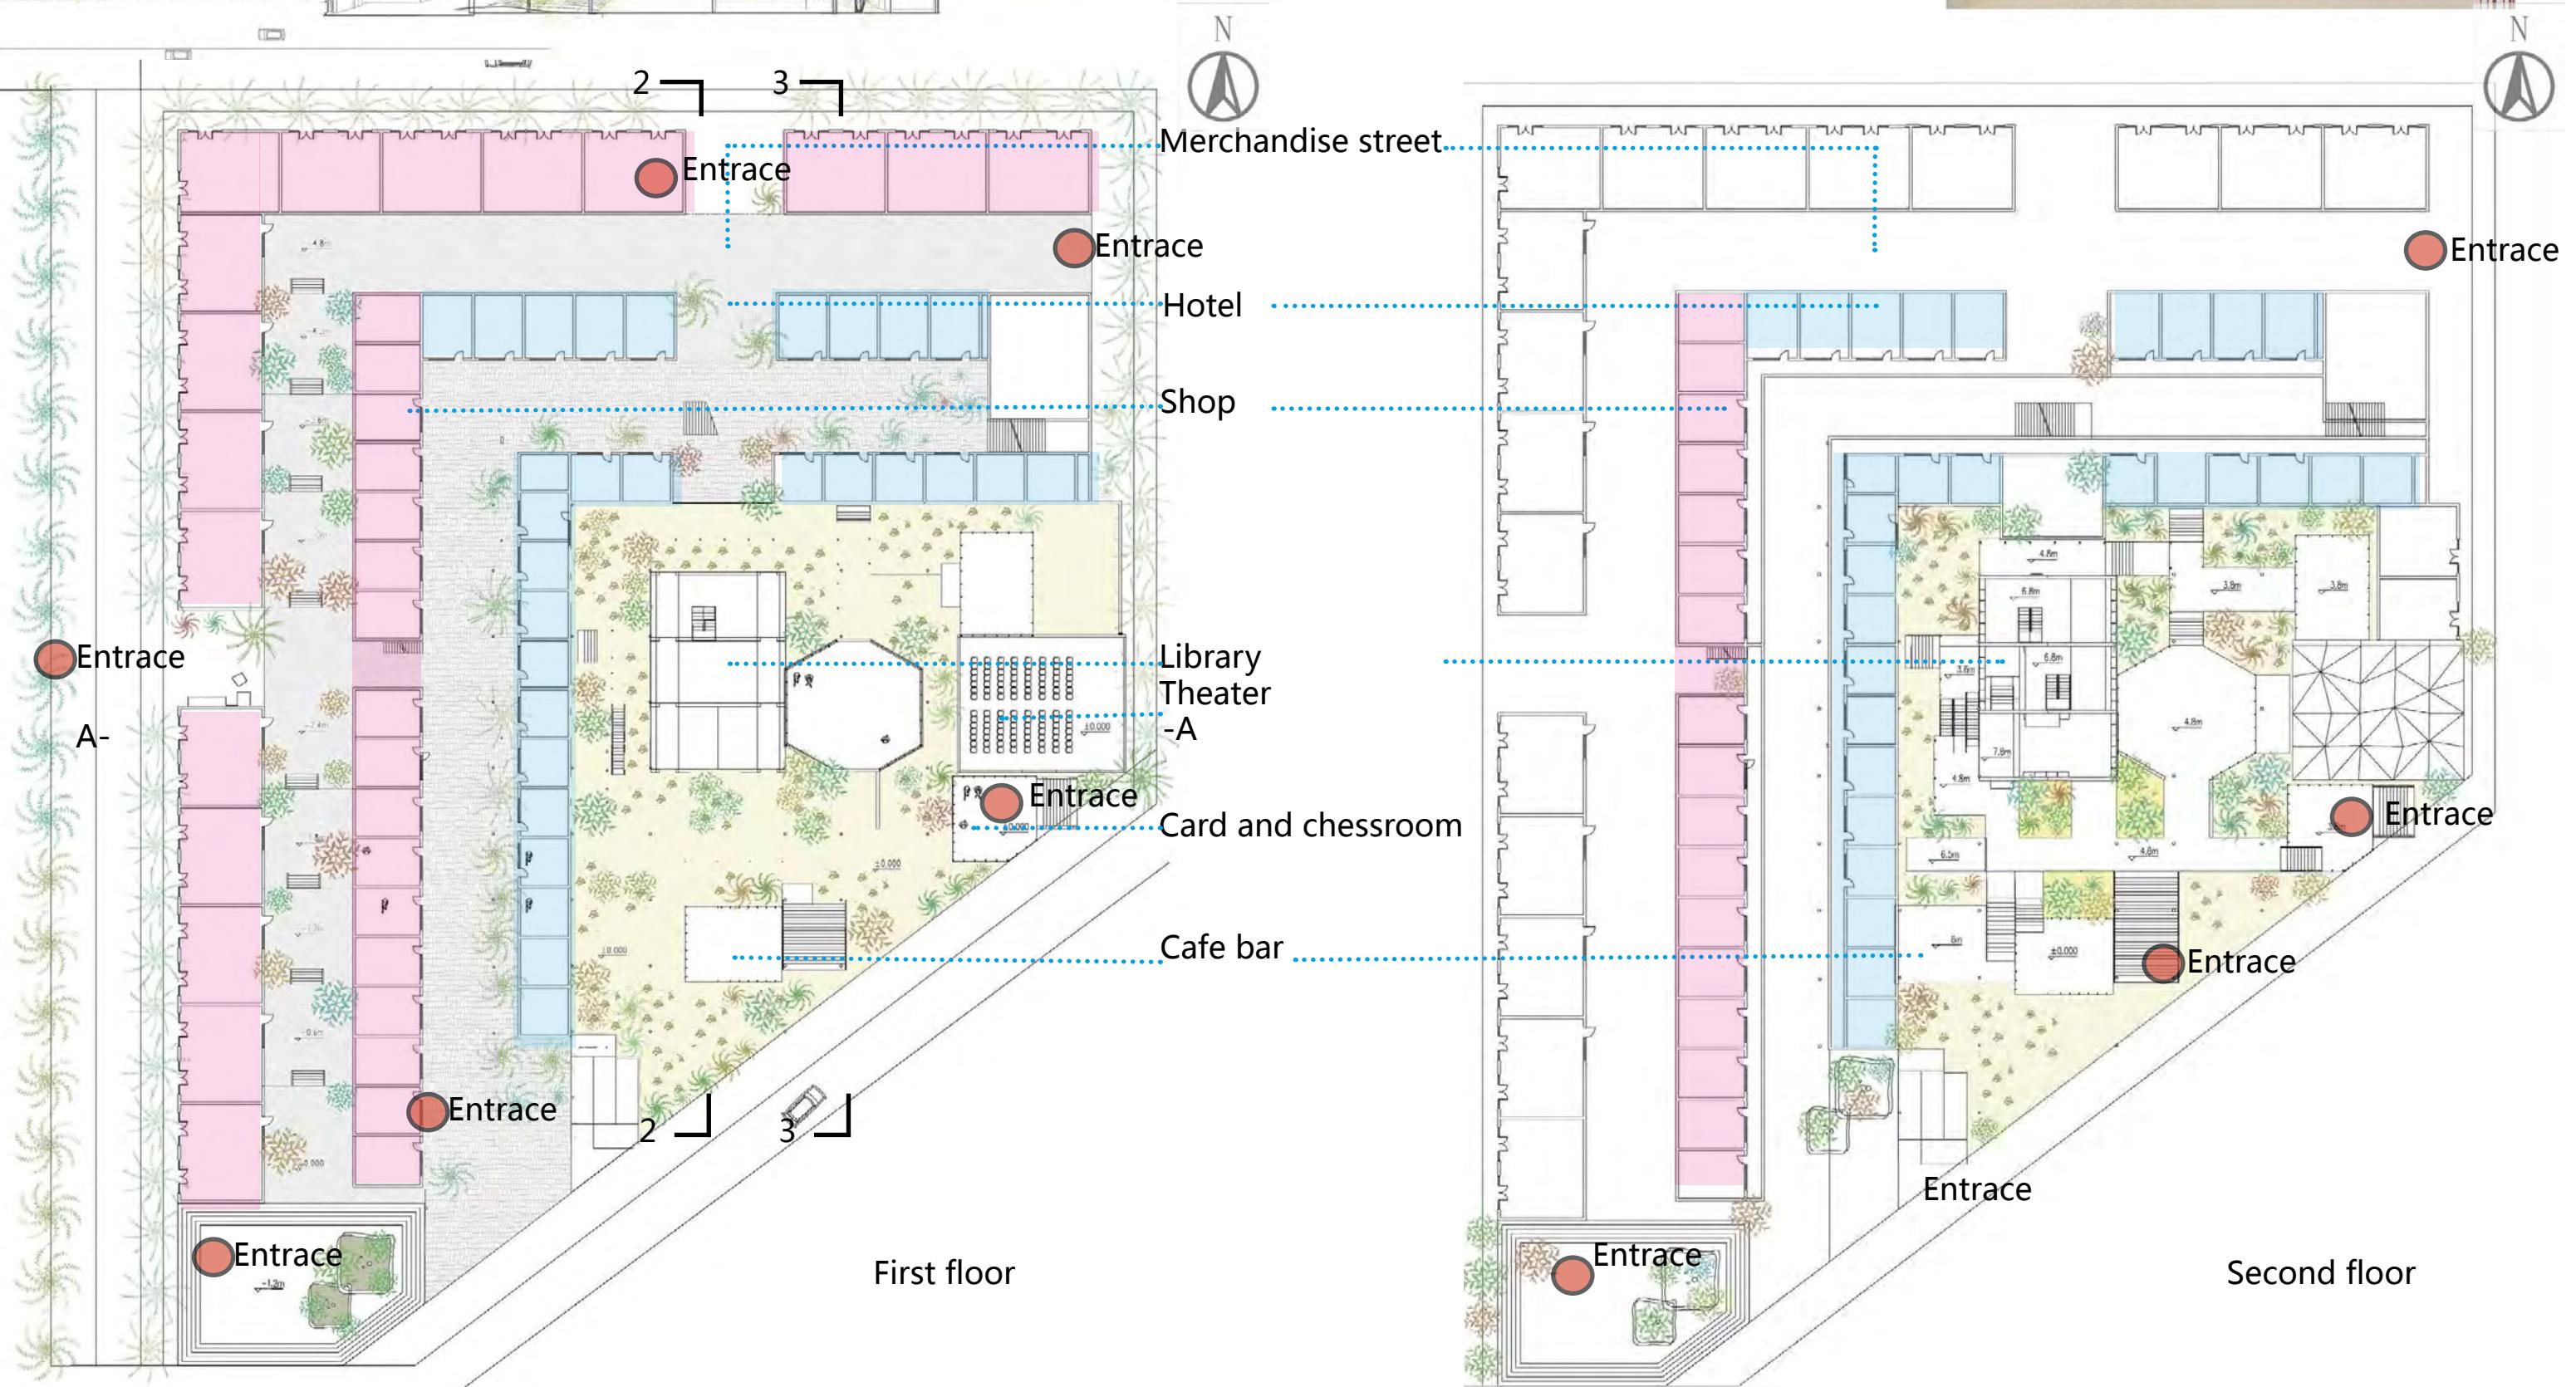




Every one will find a place to have fun: children can read books in the small library and play on the floors with different heights, tourists can buy some goods or have dinner in the old building, the elder can get together to have a chat with friends or even strangers.

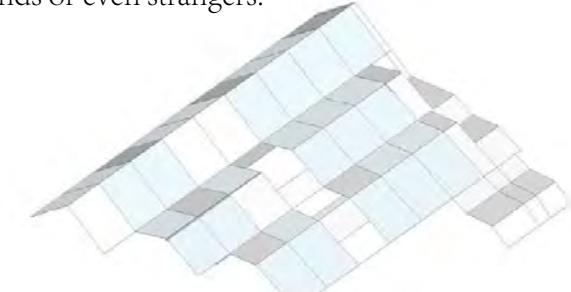


Floor with different heights. If you stand on a higher floor, you can observe the roof of old building

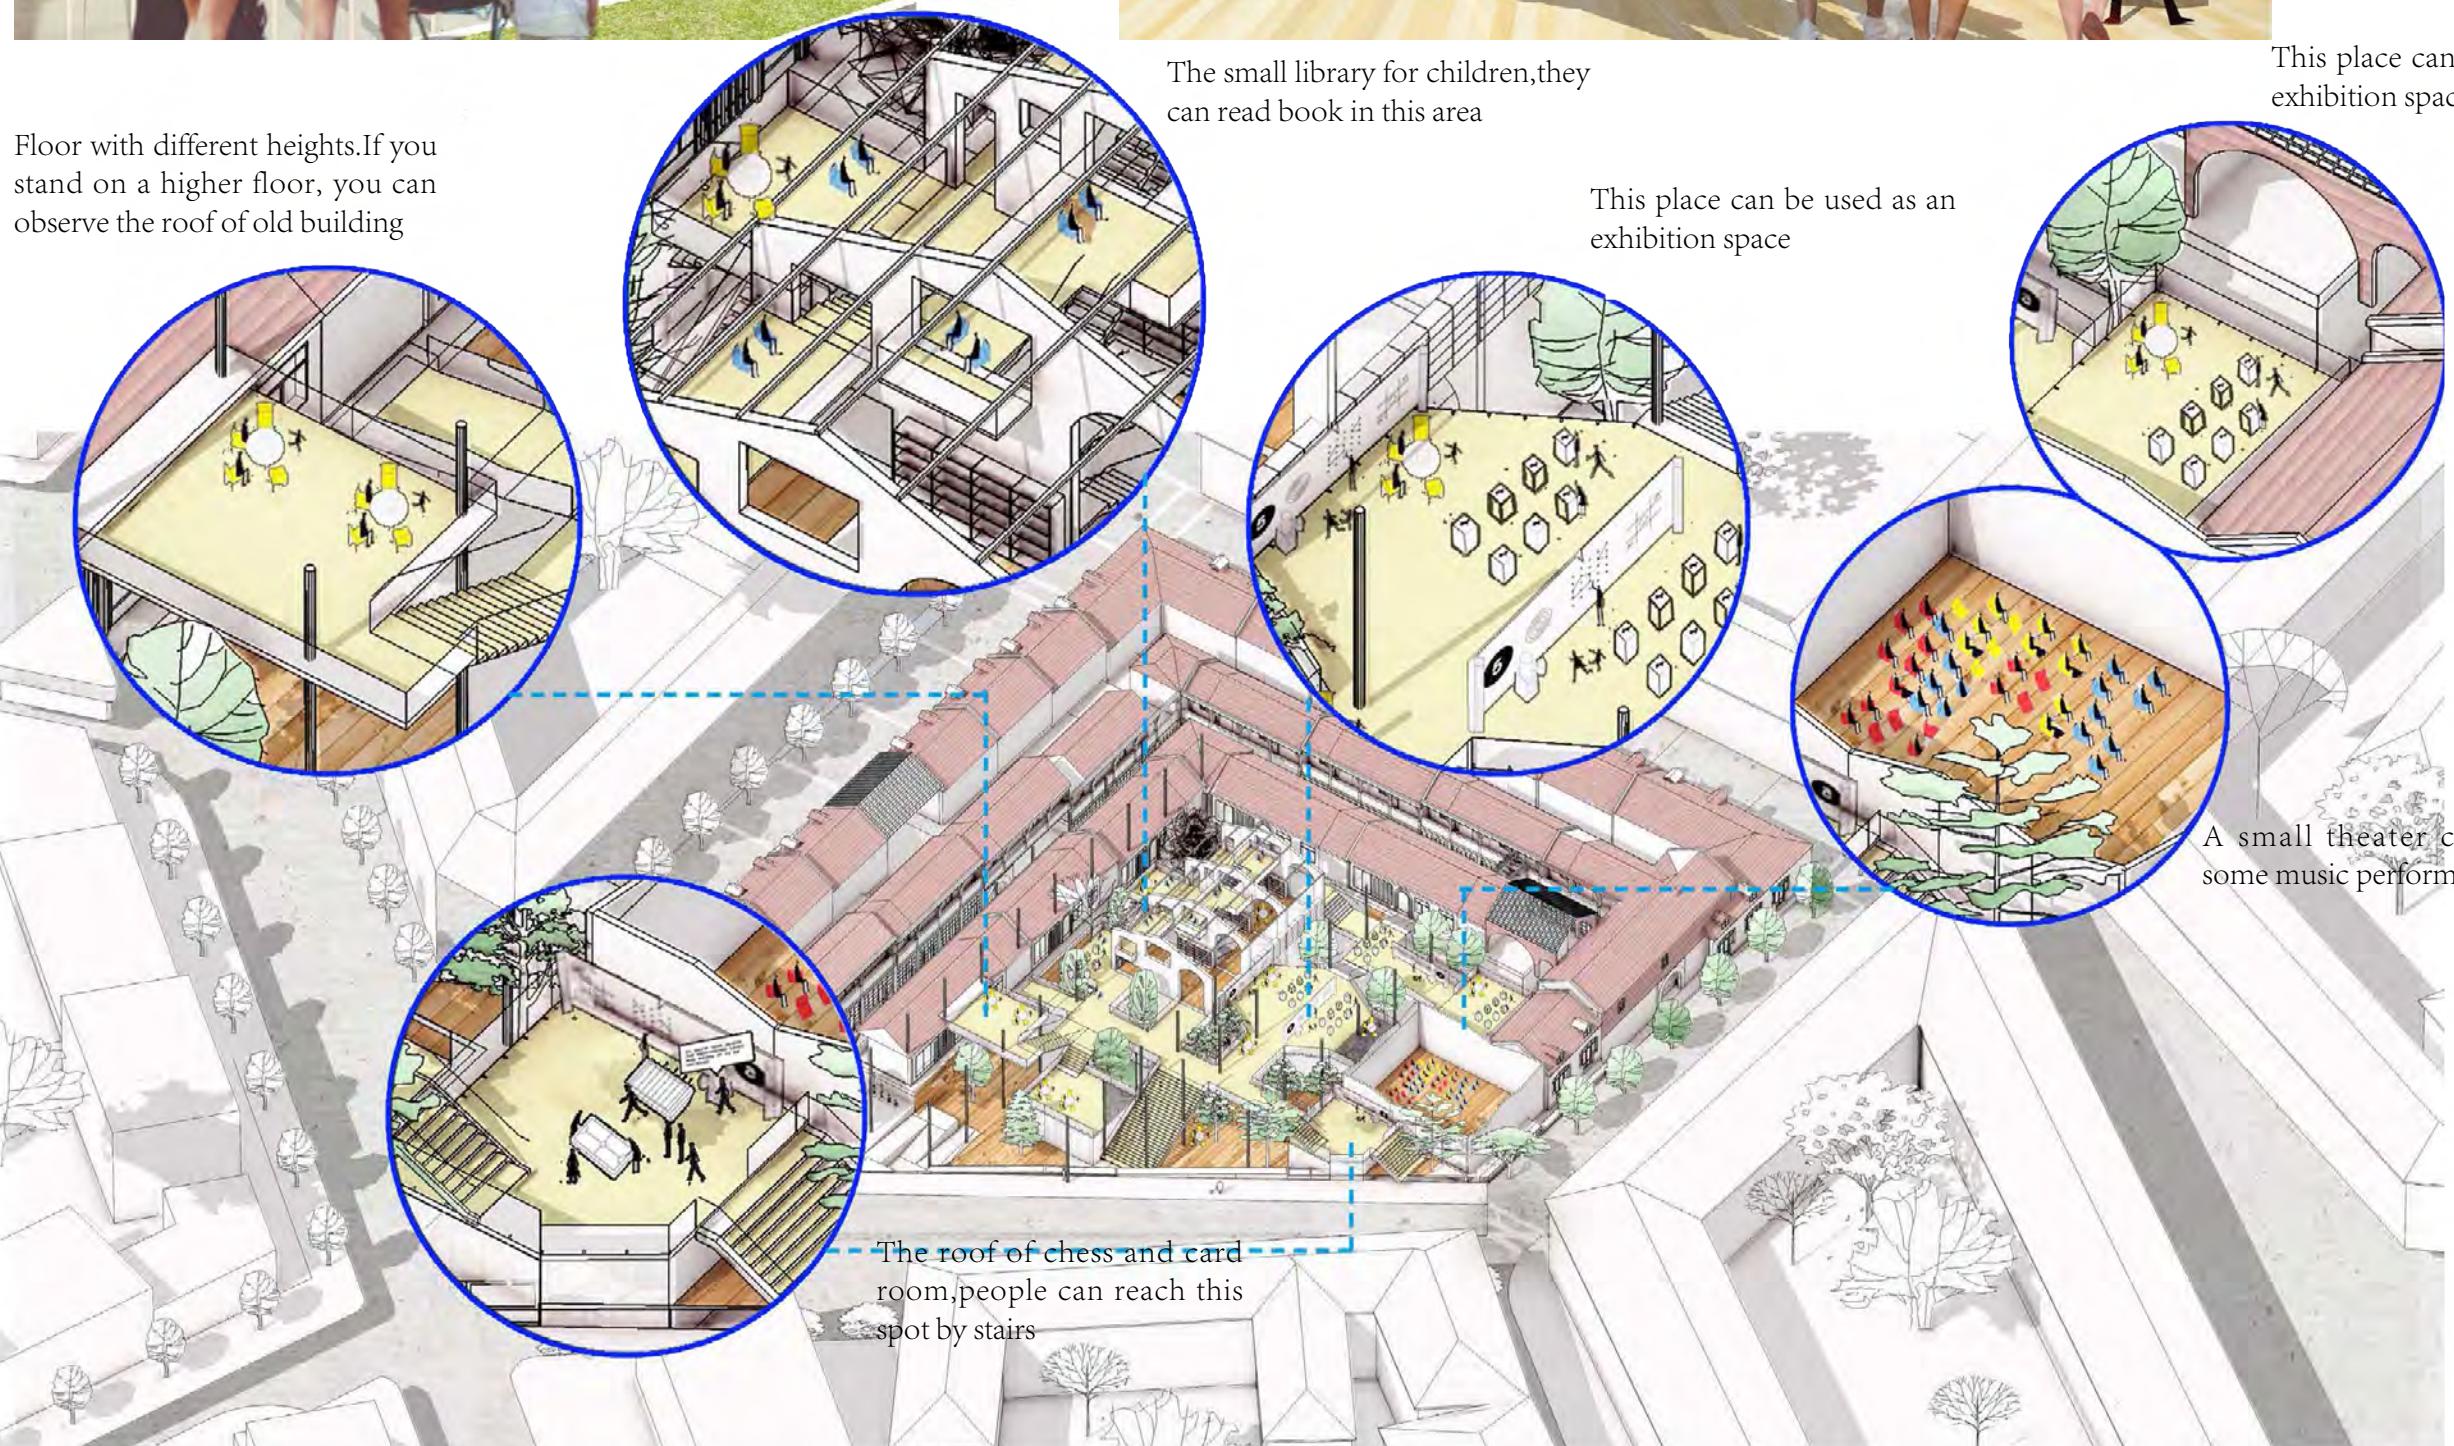


This place can be used as an exhibition space



This place can be used as an exhibition space

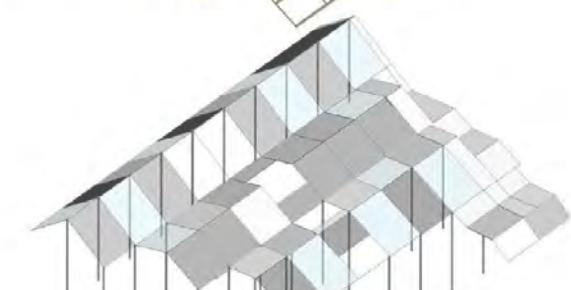

A small theater can hold some music performance

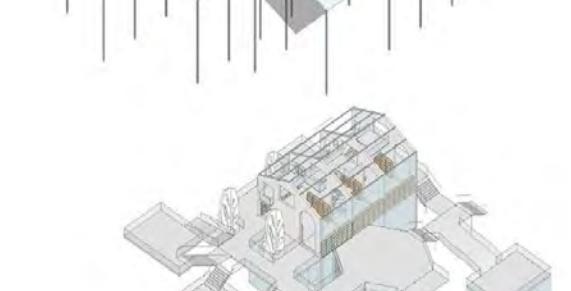


The roof of chess and card room, people can reach this spot by stairs



Between the book and trees

This is a school library located in a small woods, which has a lots of trees and a beautiful lawn. The aim of this design is try to dissolve the boundary between the interior space and the nature environment around the building. By minimizing the formal language of its architecture, the new school Library can capture the textures of the existing trees and the books within to create a cohesive experience that celebrates both.

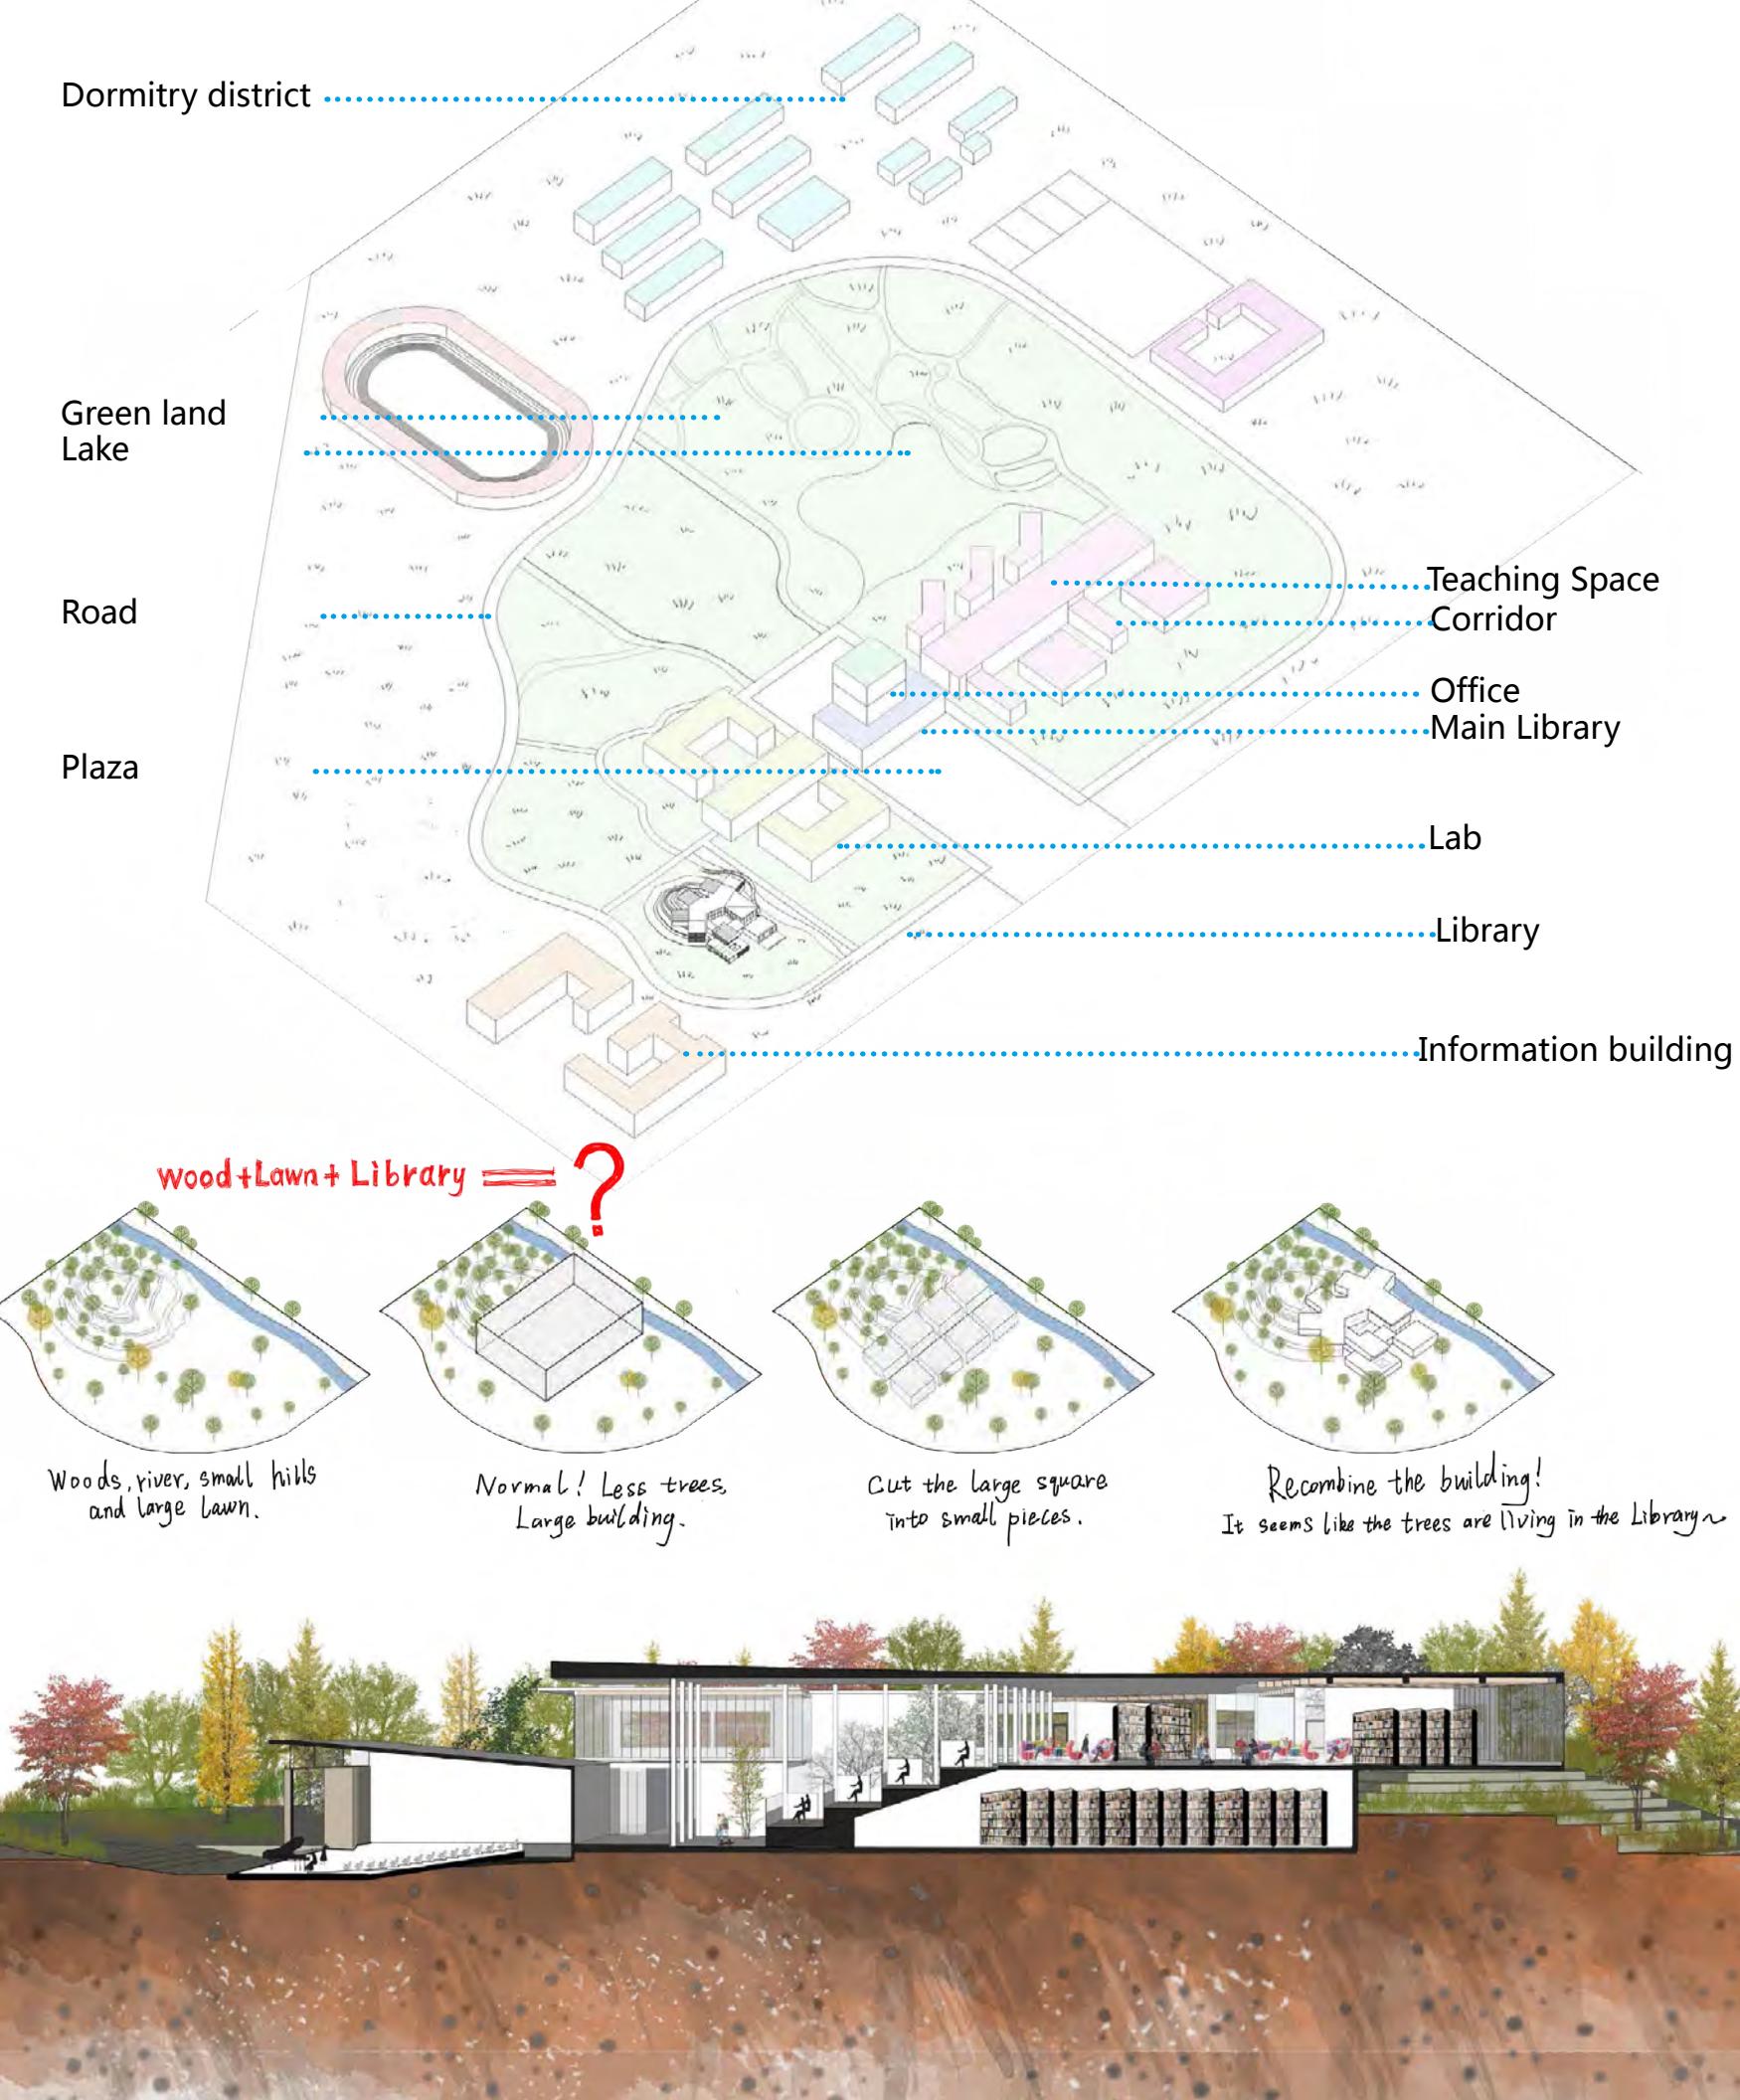



The garden between glass wall



The study space



The reading room



The south facade



Structure: pillar
Wall
U glass wall
Garden
Study space
Reading room

This library has the largest freedom to arrange the space. There is no concrete walls to distinguish the different function, the book shelves can be used as the separation and also be seen as the analogy of woods.

As the seasons change, the trees become a backdrop of color and light that creates a variety of experiences.

Architecture park in the city

Architecture in Transformation Unexpected City

繁华城市中的建筑公园



Site: Hong Kong west road and two boxes six-way interchange

Area: 9100m² (130*70)

Elevation difference: 8m


Site: In fact, it is in the most prosperous Hong Kong west road. Qingdao Hong Kong west road south is commercial buildings, more famous buildings, such as Renaissance harbour view north is more high-end residential, west near badaguan buildings. Population density is big. The crowd around the lack of a public nature of the park, the idea to build a park here to meet people's needs.



What is architecture park?

A predominantly building space, the lack of a park in the city populated area environment, through the architectural space to create a park, provide people with leisure, the emergence of building the park can greatly solve the building city of highly populated areas lack of status quo of the park.

Status quo park: most plants are given priority to with green space, with beautiful environment provide people with leisure function, but the downside is also evident is the general park often requires a very large area, in the city populated area tend not to have a large area of the park, so building the park of the moment can be a good solution to this problem, use a small area of the space inside the prosperous areas to create a building parks provide people with leisure function.

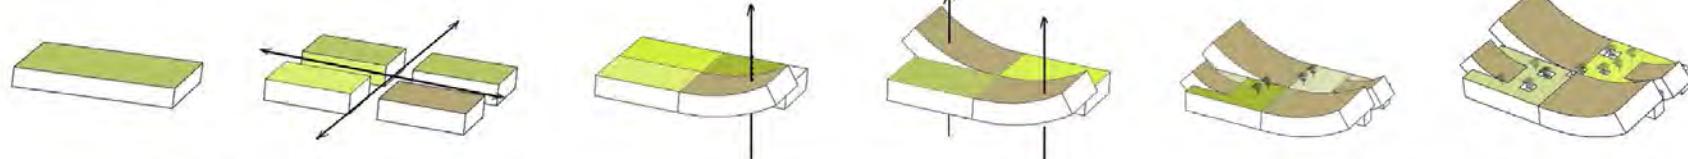

The average segmentation base area


Both sides cocking build semi-enclosed space

Ground tree sink and dropped to the ground, underground green space



Concept: Trace (痕迹)


Theme: architecture park in the city

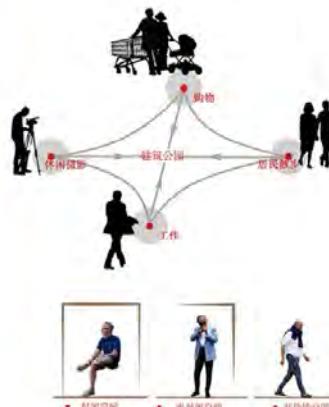

Building the park from the concept of trace, feel the ups and downs of the earth, space constructed by the changes, and building the park is a communication connection photography, leisure shopping consumption, work in business, an aggregation of people walking and other functions


By rolling construction space is divided into three types: closed space, semi-enclosed space, open space, building interior space is confined space by building wall divided internal space and external, semi-enclosed space is under construction and the earth produced by space, there are both building envelopes and the earth to space to surround close so is a semi-enclosed space, open space is part of the earth between buildings, the space is fully open, consists of a large number of green plants, and have subsided underground entrance, can enter the underground space





Atmosphere building a park five parts, the four part and an underground parts on the ground, the ground four parts respectively are 1, 2, 3, 4 # hall, hall is the main building, 1 area is the largest, the highest height, is the center of the building, no. 1 museum exhibition is reading and green plants, are the two main functions of 2 hall is the second largest in the buildings, all function is green plants show, hall no. 3 is the smallest, is to provide food and rest the whole building park in the main place, museum is a building across the road, 4 internal mainly provide exhibition, the rest of the space will be merged into a mental picture of traffic flow, the fifth part is the underground buildings, underground buildings is the rest four parts first, second and in the ground to build a park space, to form the underground, road surface, roof, building three-dimensional space

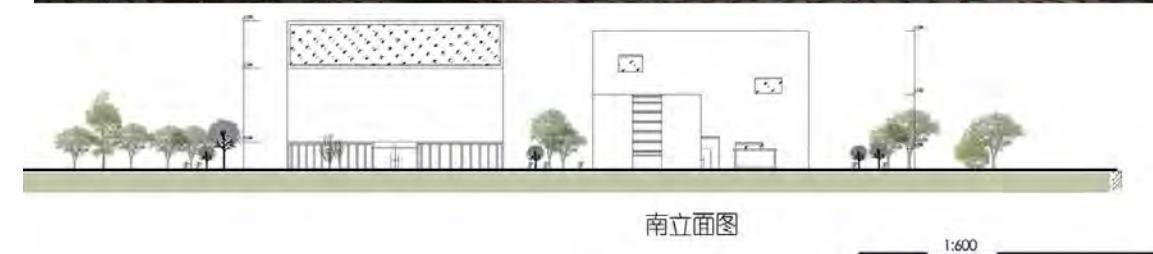

南立面图


1:600

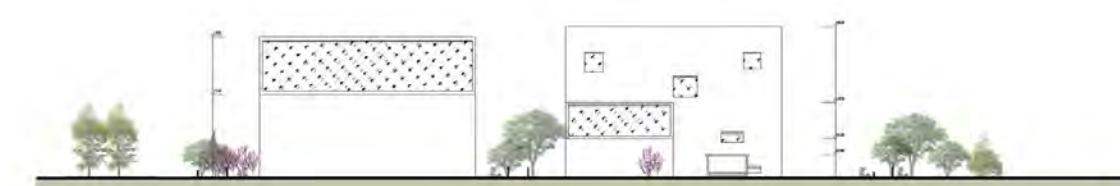

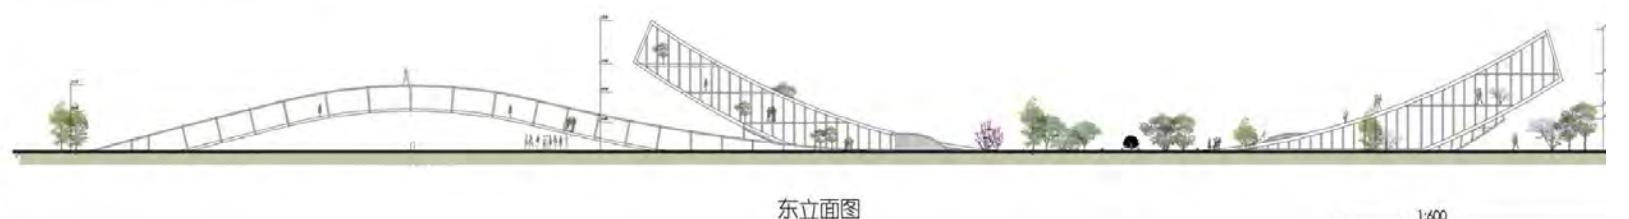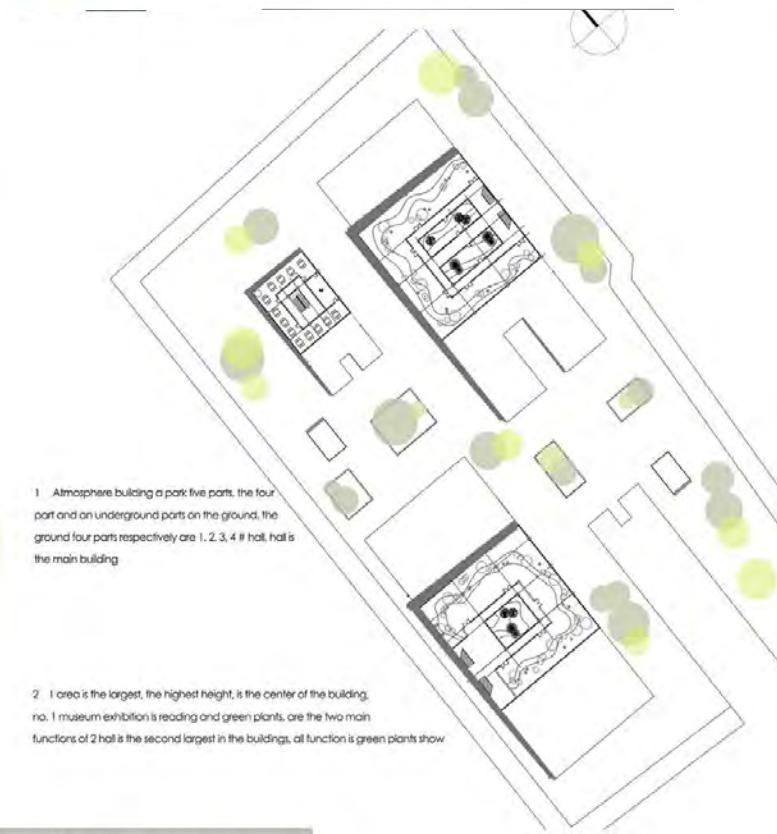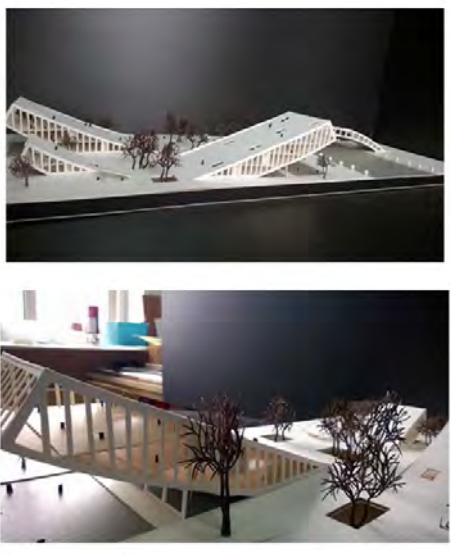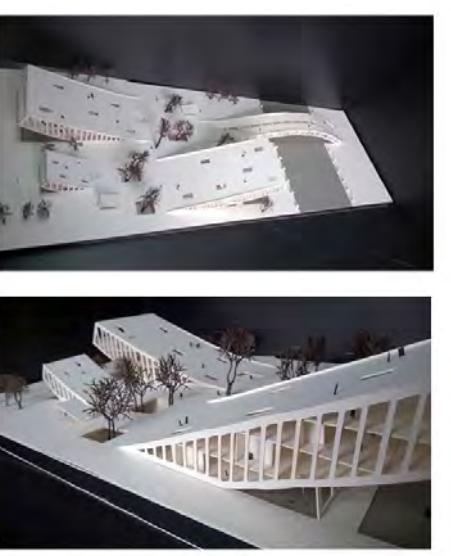

建筑公园一个氛围五部分，由四个地上部分和一个地下部分组成。地上四部分分别是1、2、3、4号馆，1号馆是主建筑，面积最大，高度最高，是整个建筑群的中心。一号馆的功能主要是阅读和绿色植物展览。二号馆是整个建筑群中面积第二大的，全部功能是绿色植物展览。三号馆是面积最小的，是提供整个建筑公园中餐饮休息的主要场所，四号馆是一个四面透光建筑。内部主要提供展览、休息的空间将川流不息的车流汇成一部画卷。第五部分是地下建筑。地下建筑首先是将其余四部分建筑联系起来，其次又在地下塑造一个公园空间，形成地下、路面、屋顶，三维的空间建筑。

Atmosphere building a park five parts, the four part and on underground parts on the ground, the ground four parts respectively are 1, 2, 3, 4 # hall, hall is the main building, 1 area is the largest, the highest height, is the center of the building, no. 1 museum exhibition is reading and green plants, are the two main functions of 2 hall is the second largest in the buildings, all function is green plants show, hall no. 3 is the smallest, is to provide food and rest the whole building park in the main place, museum is a building across the road, 4 internal mainly provide exhibition, the rest of the space will be merged into a mental picture of traffic flow, the fifth part is the underground buildings, underground buildings is the rest four parts first, second and in the ground to build a park space, to form the underground, road surface, roof, building three-dimensional space

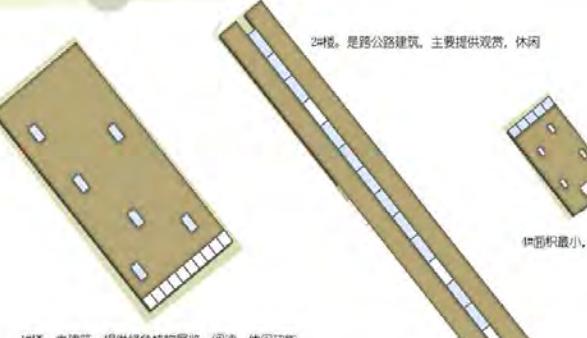

Urban design

This design is trying to rebuild an old fishing port in Qingdao, Shazikou. The scene near this region is beautiful. With the development

of modern society, people in this area don't have to live on fishing. They could rebuild this area and give more function to the seashore.

Such as hotel, restaurant, and store.

current situation



village


fishing boat



warehouse




mountain line and architecture line

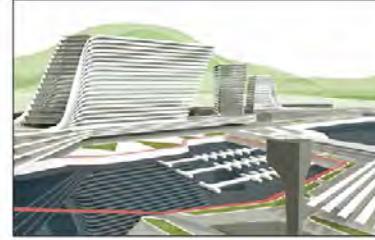

dense

sparse

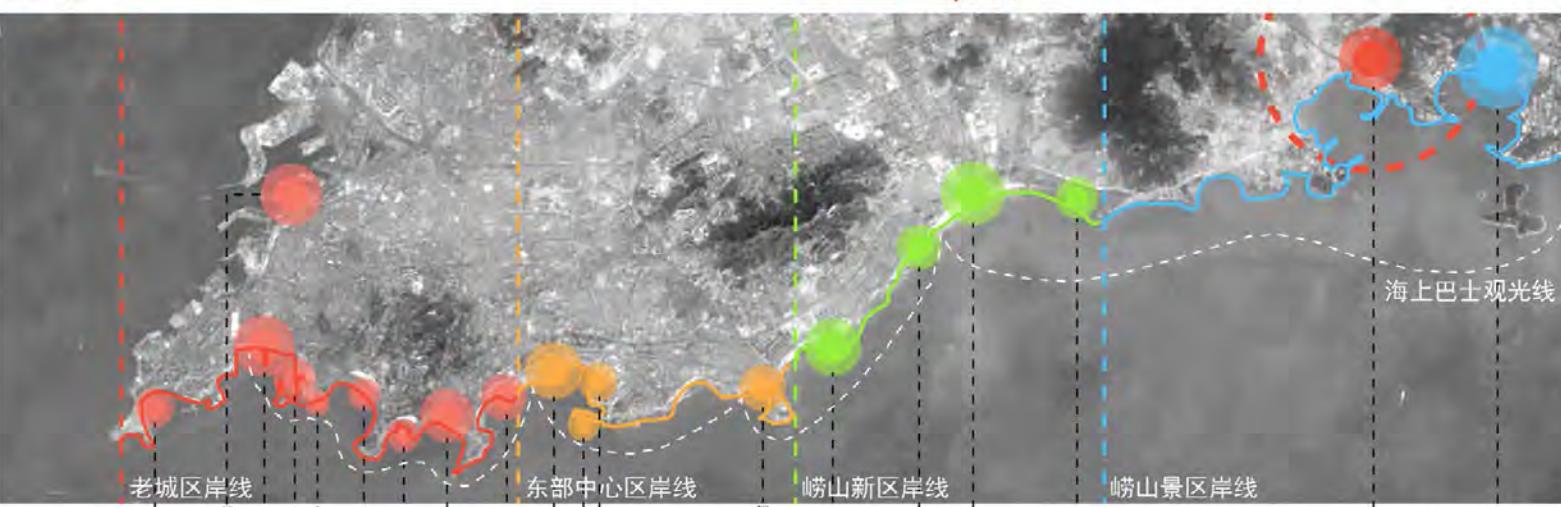

main spot
hot spot
transition spot
normal spot

团岛 ← → 太平角六路 太平角六路 ← → 麦岛 麦岛 ← → 石老人 石老人 ← → 岱山

construction time 1980s 栈桥 1890s-1930s 五四广场 1992 重点区域 2000s 沙子口

main function 家庭生活、购物、娱乐、餐饮

家庭生活、购物、娱乐、餐饮

家庭生活、购物、娱乐、餐饮

……?



scenery spot

城市滨海天际线

Sky line near the sea

traditional fishing village

传统渔村


渔家宴及民宿






corridor in the air

High-rise hotel

综合办公

National fishing port

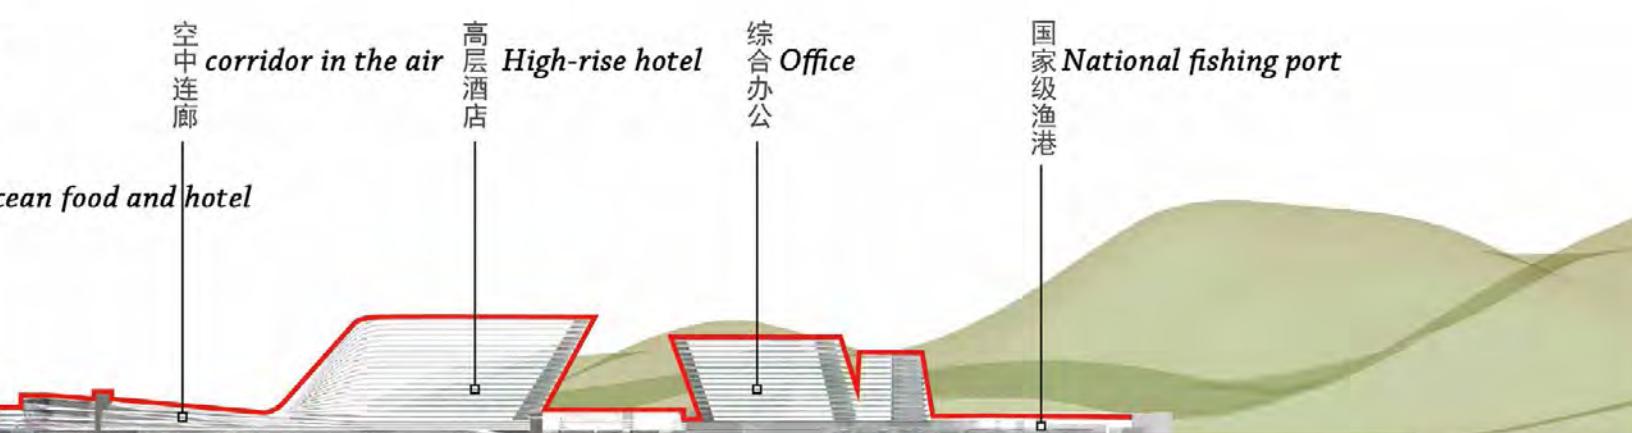

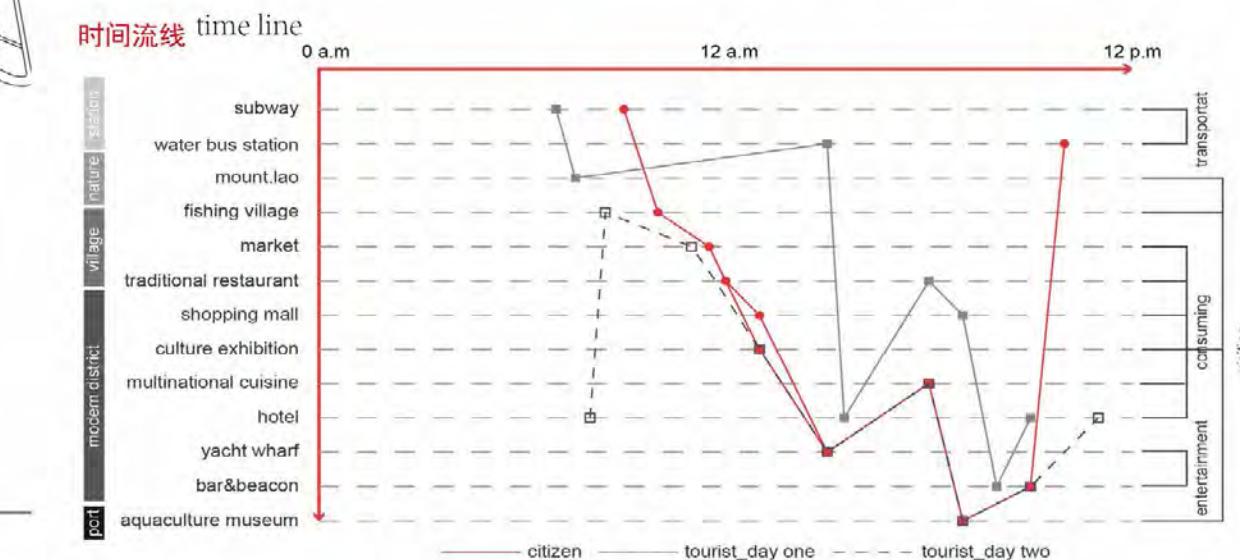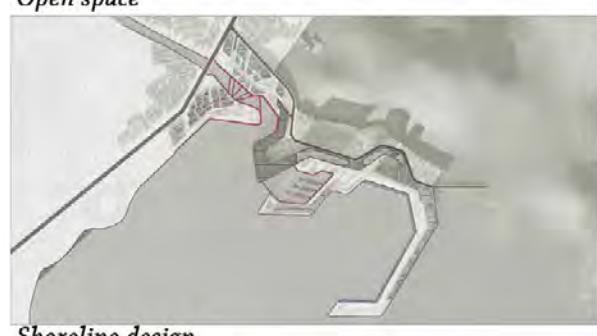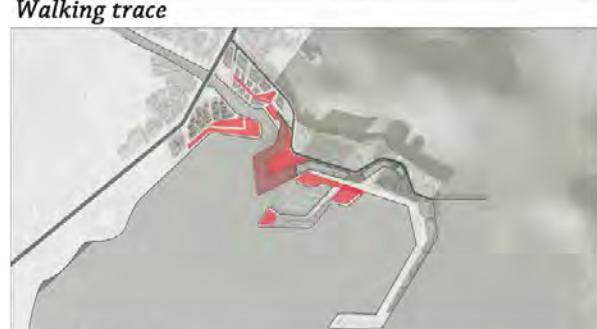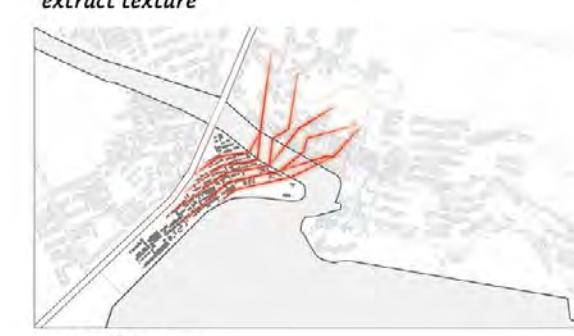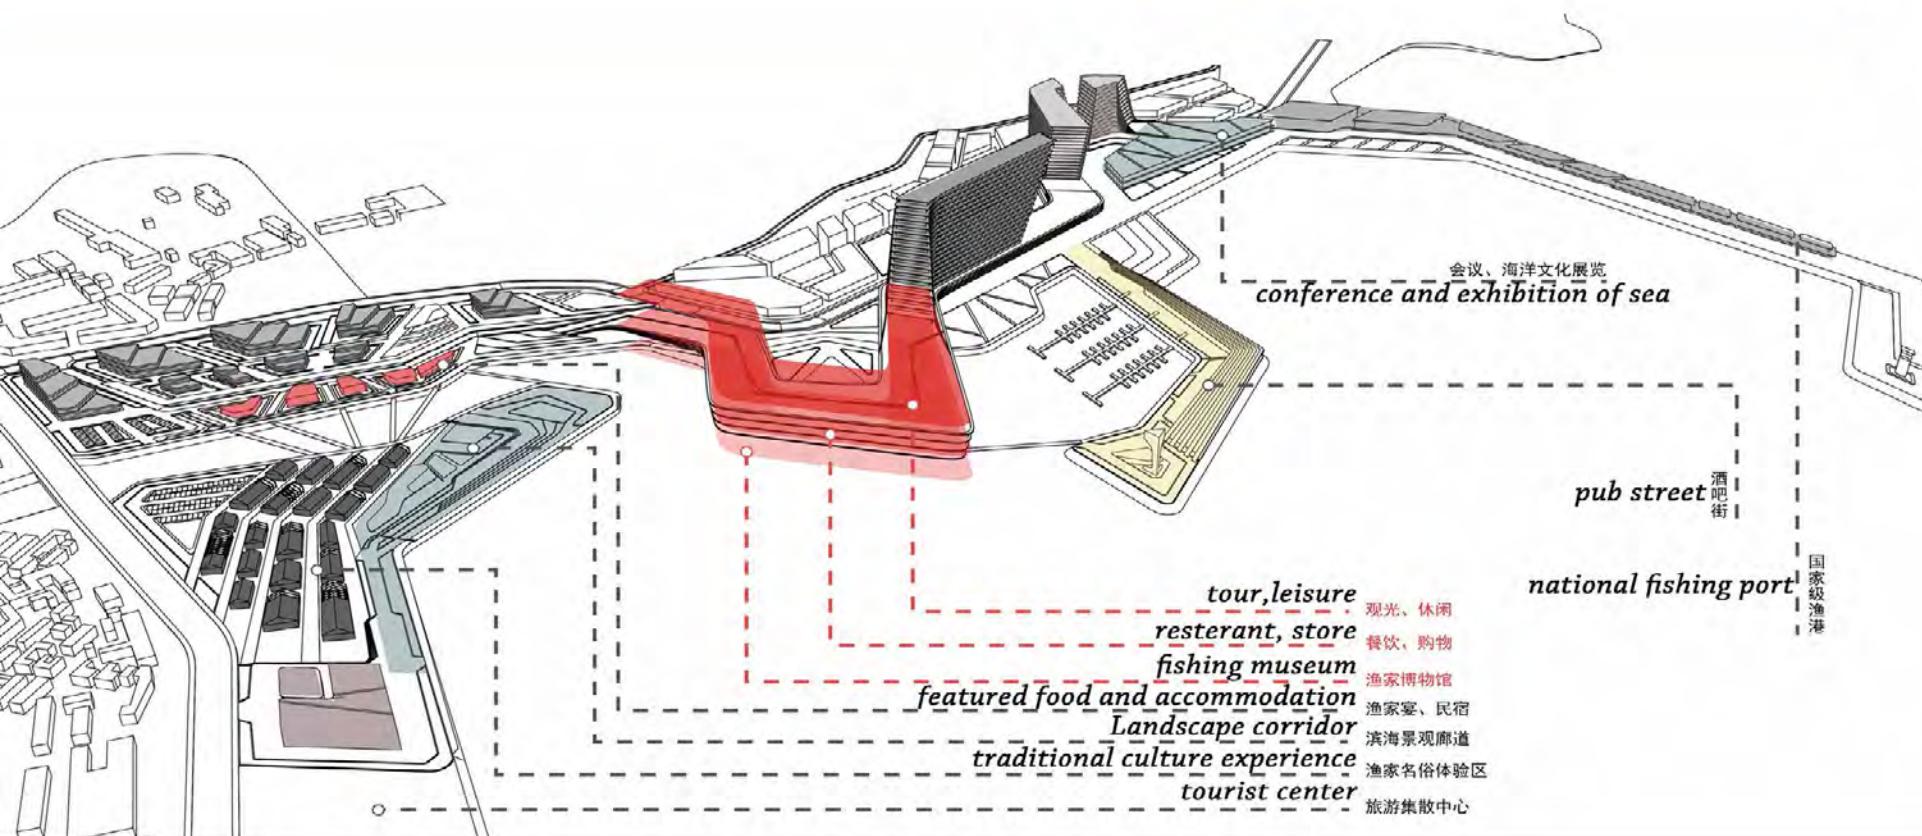

Other works




Other works



Other works


Mini community center

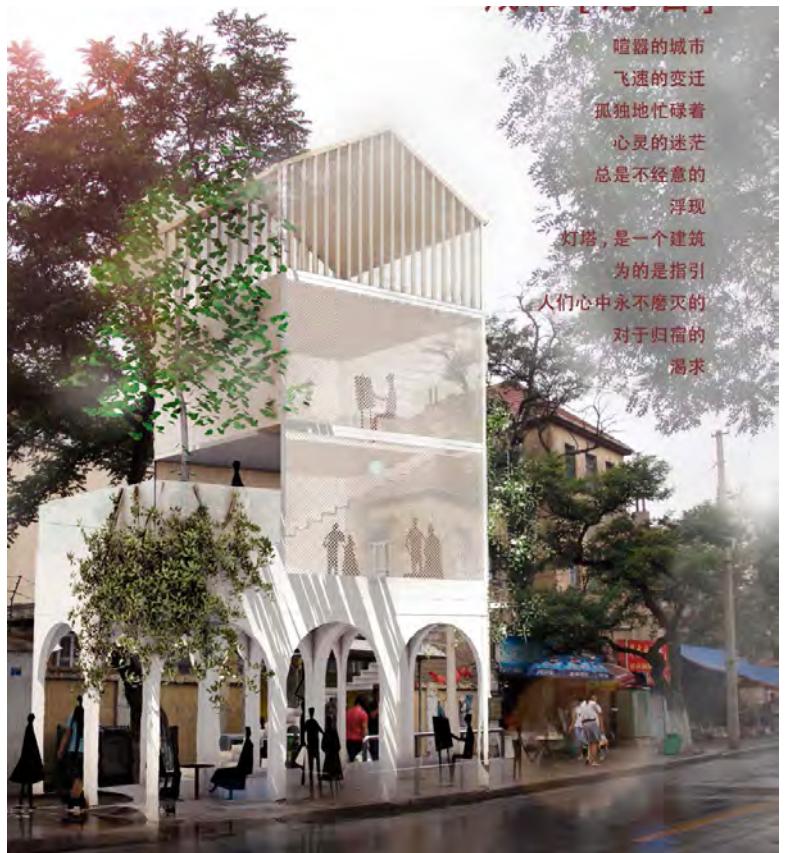

Wood architecture



Landscape design

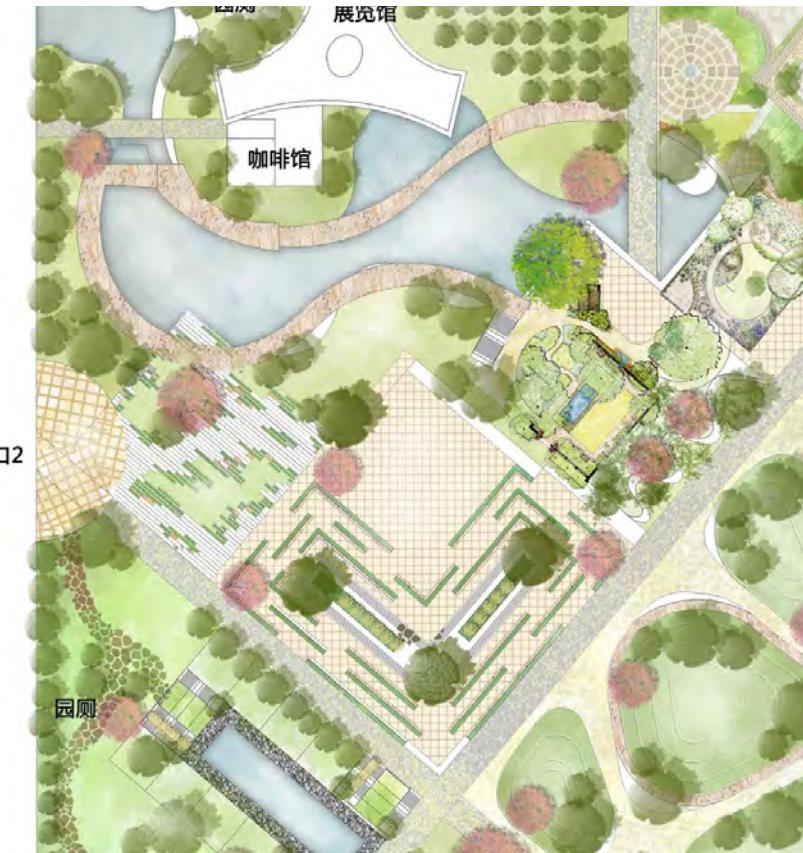

Photography

